


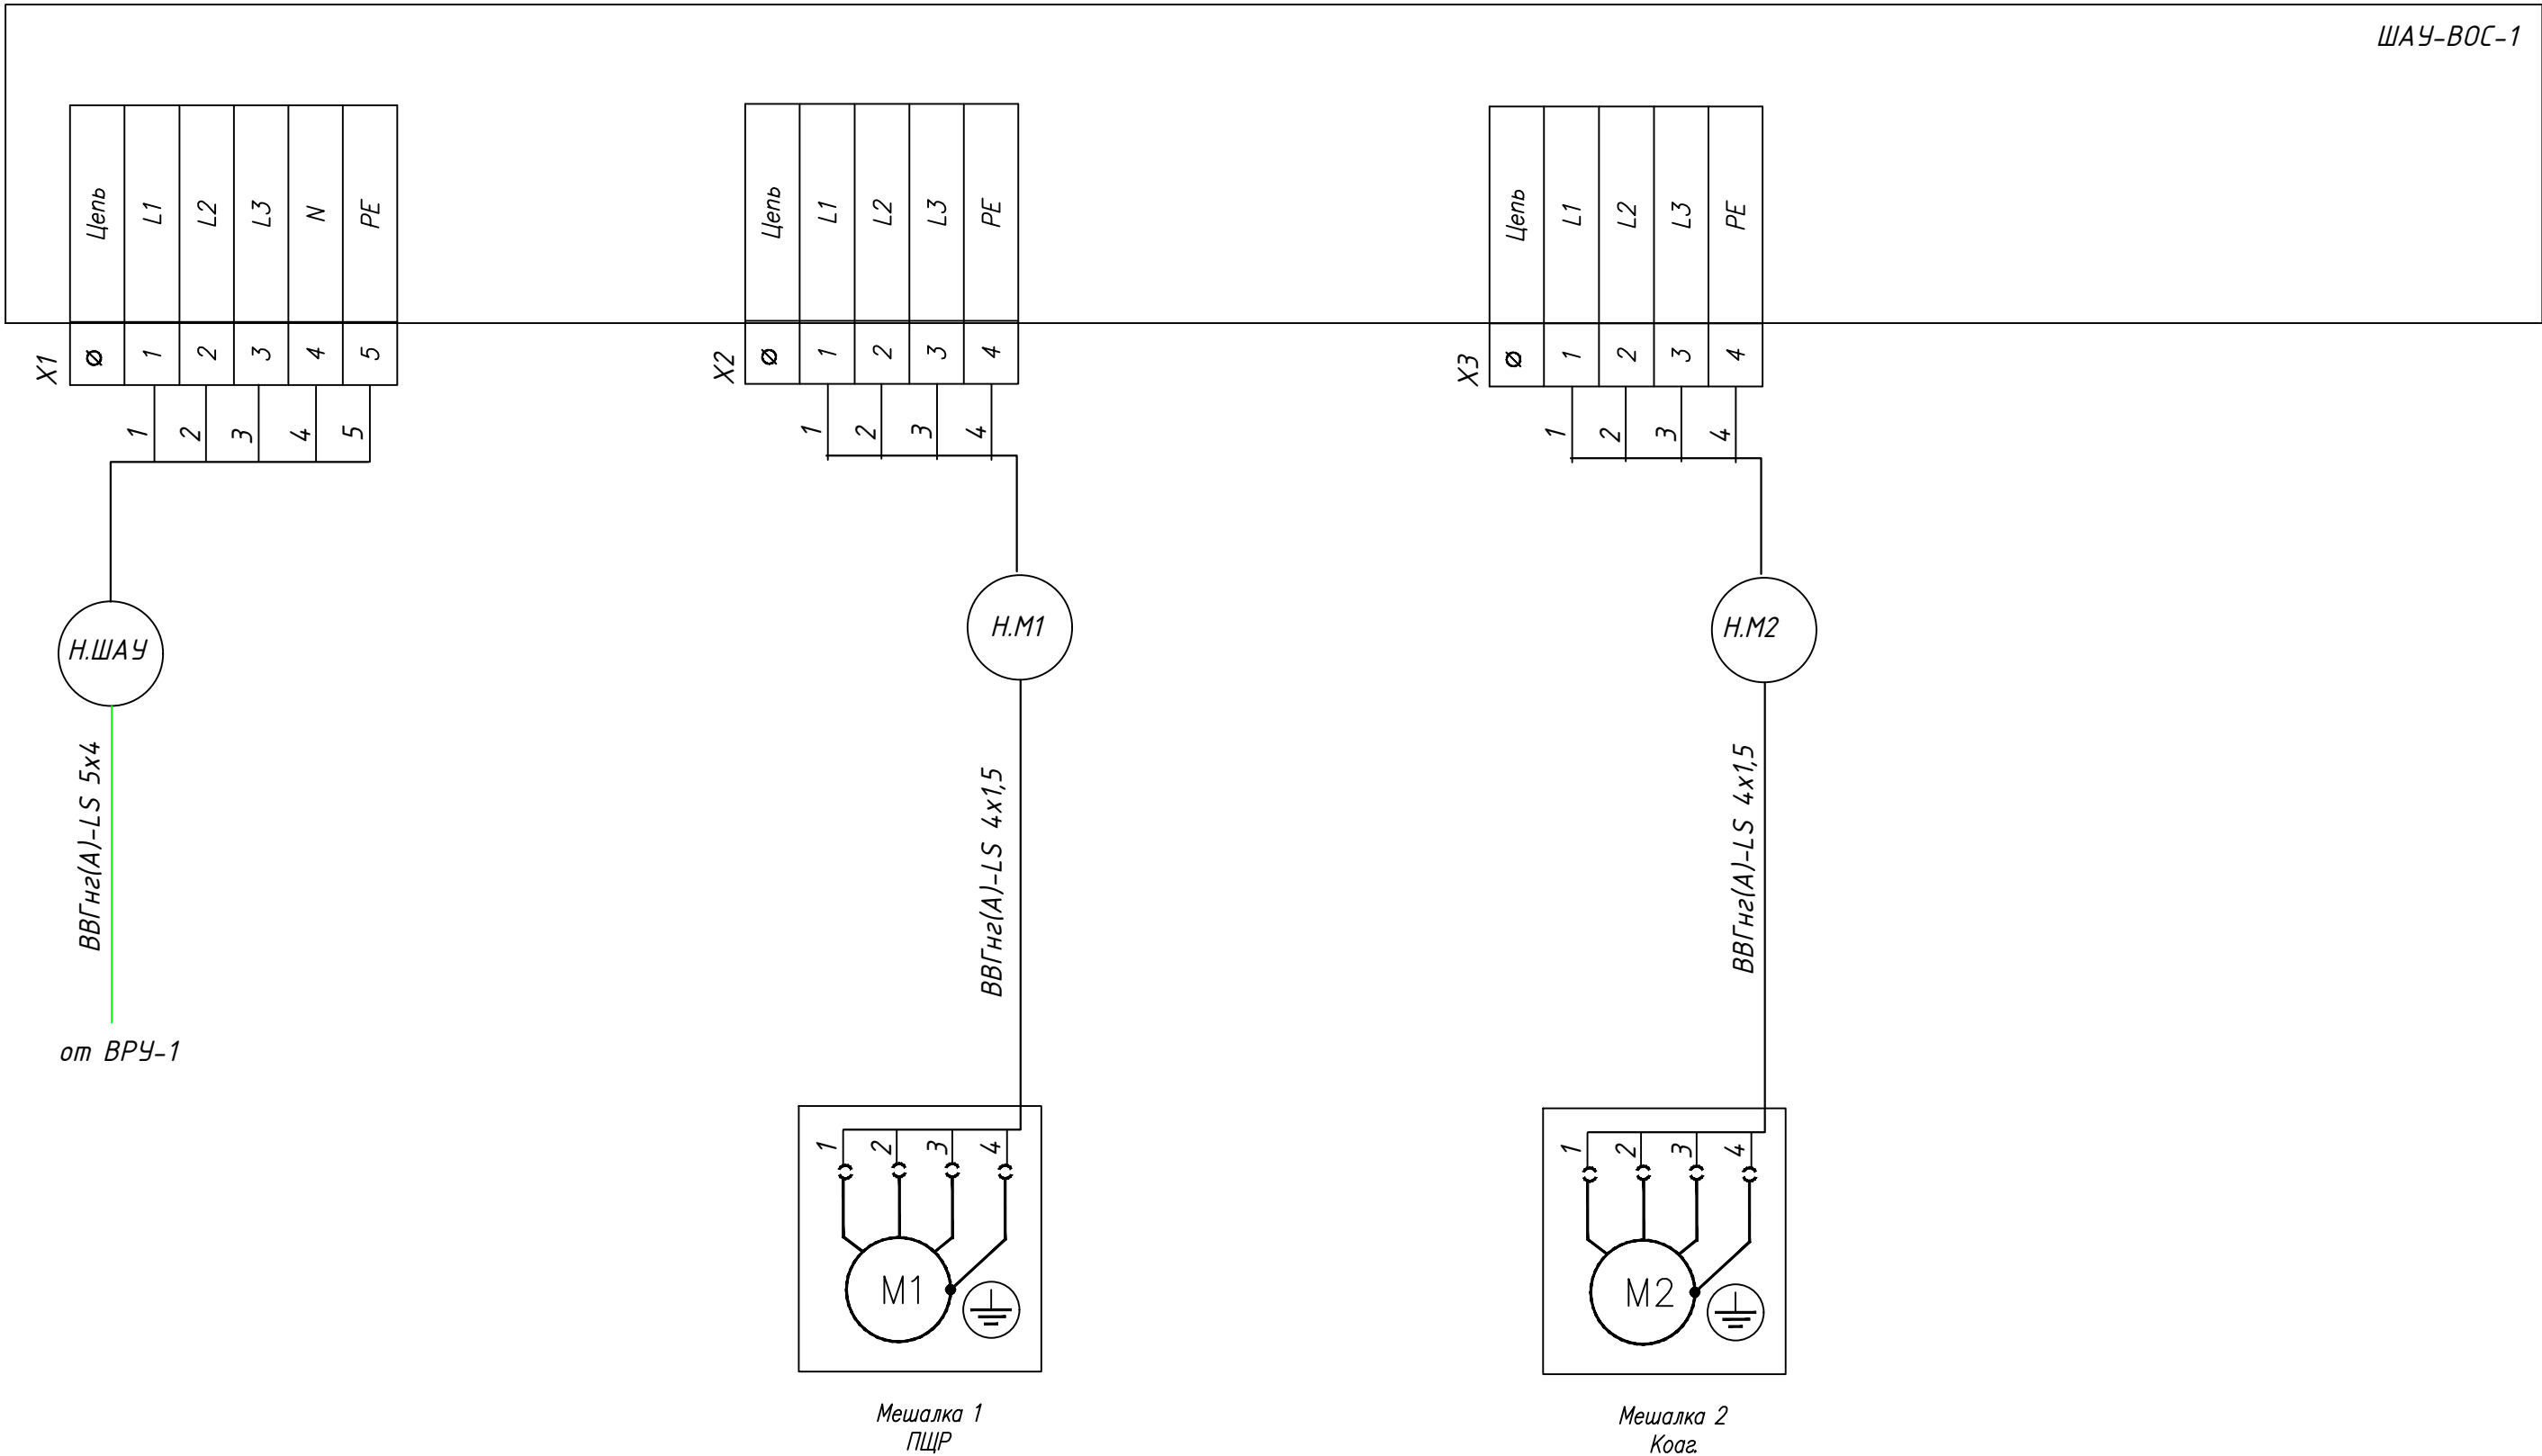

						14192.012/2024-АТХ				
						«Модернизация объекта «Здание воочистных сооружений» в с. Панаевск»				
Изм.	Кол.уч.	Лист	N док.	Подп.	Дата	Автоматизация технологии	Стадия	Лист	Листов	
Разраб.	Бакланов				04.25		Р	5.1	10	
Проверил	Никулин				04.25					
Н. контр.	Шамова				04.25	ШАУ-ВОС-1 Схема внешних соединений	ООО "МСБ"			
ГИП	Усвятцев				04.25					