


Инв.№подл.	Подпись и дата	Взам.инв.№

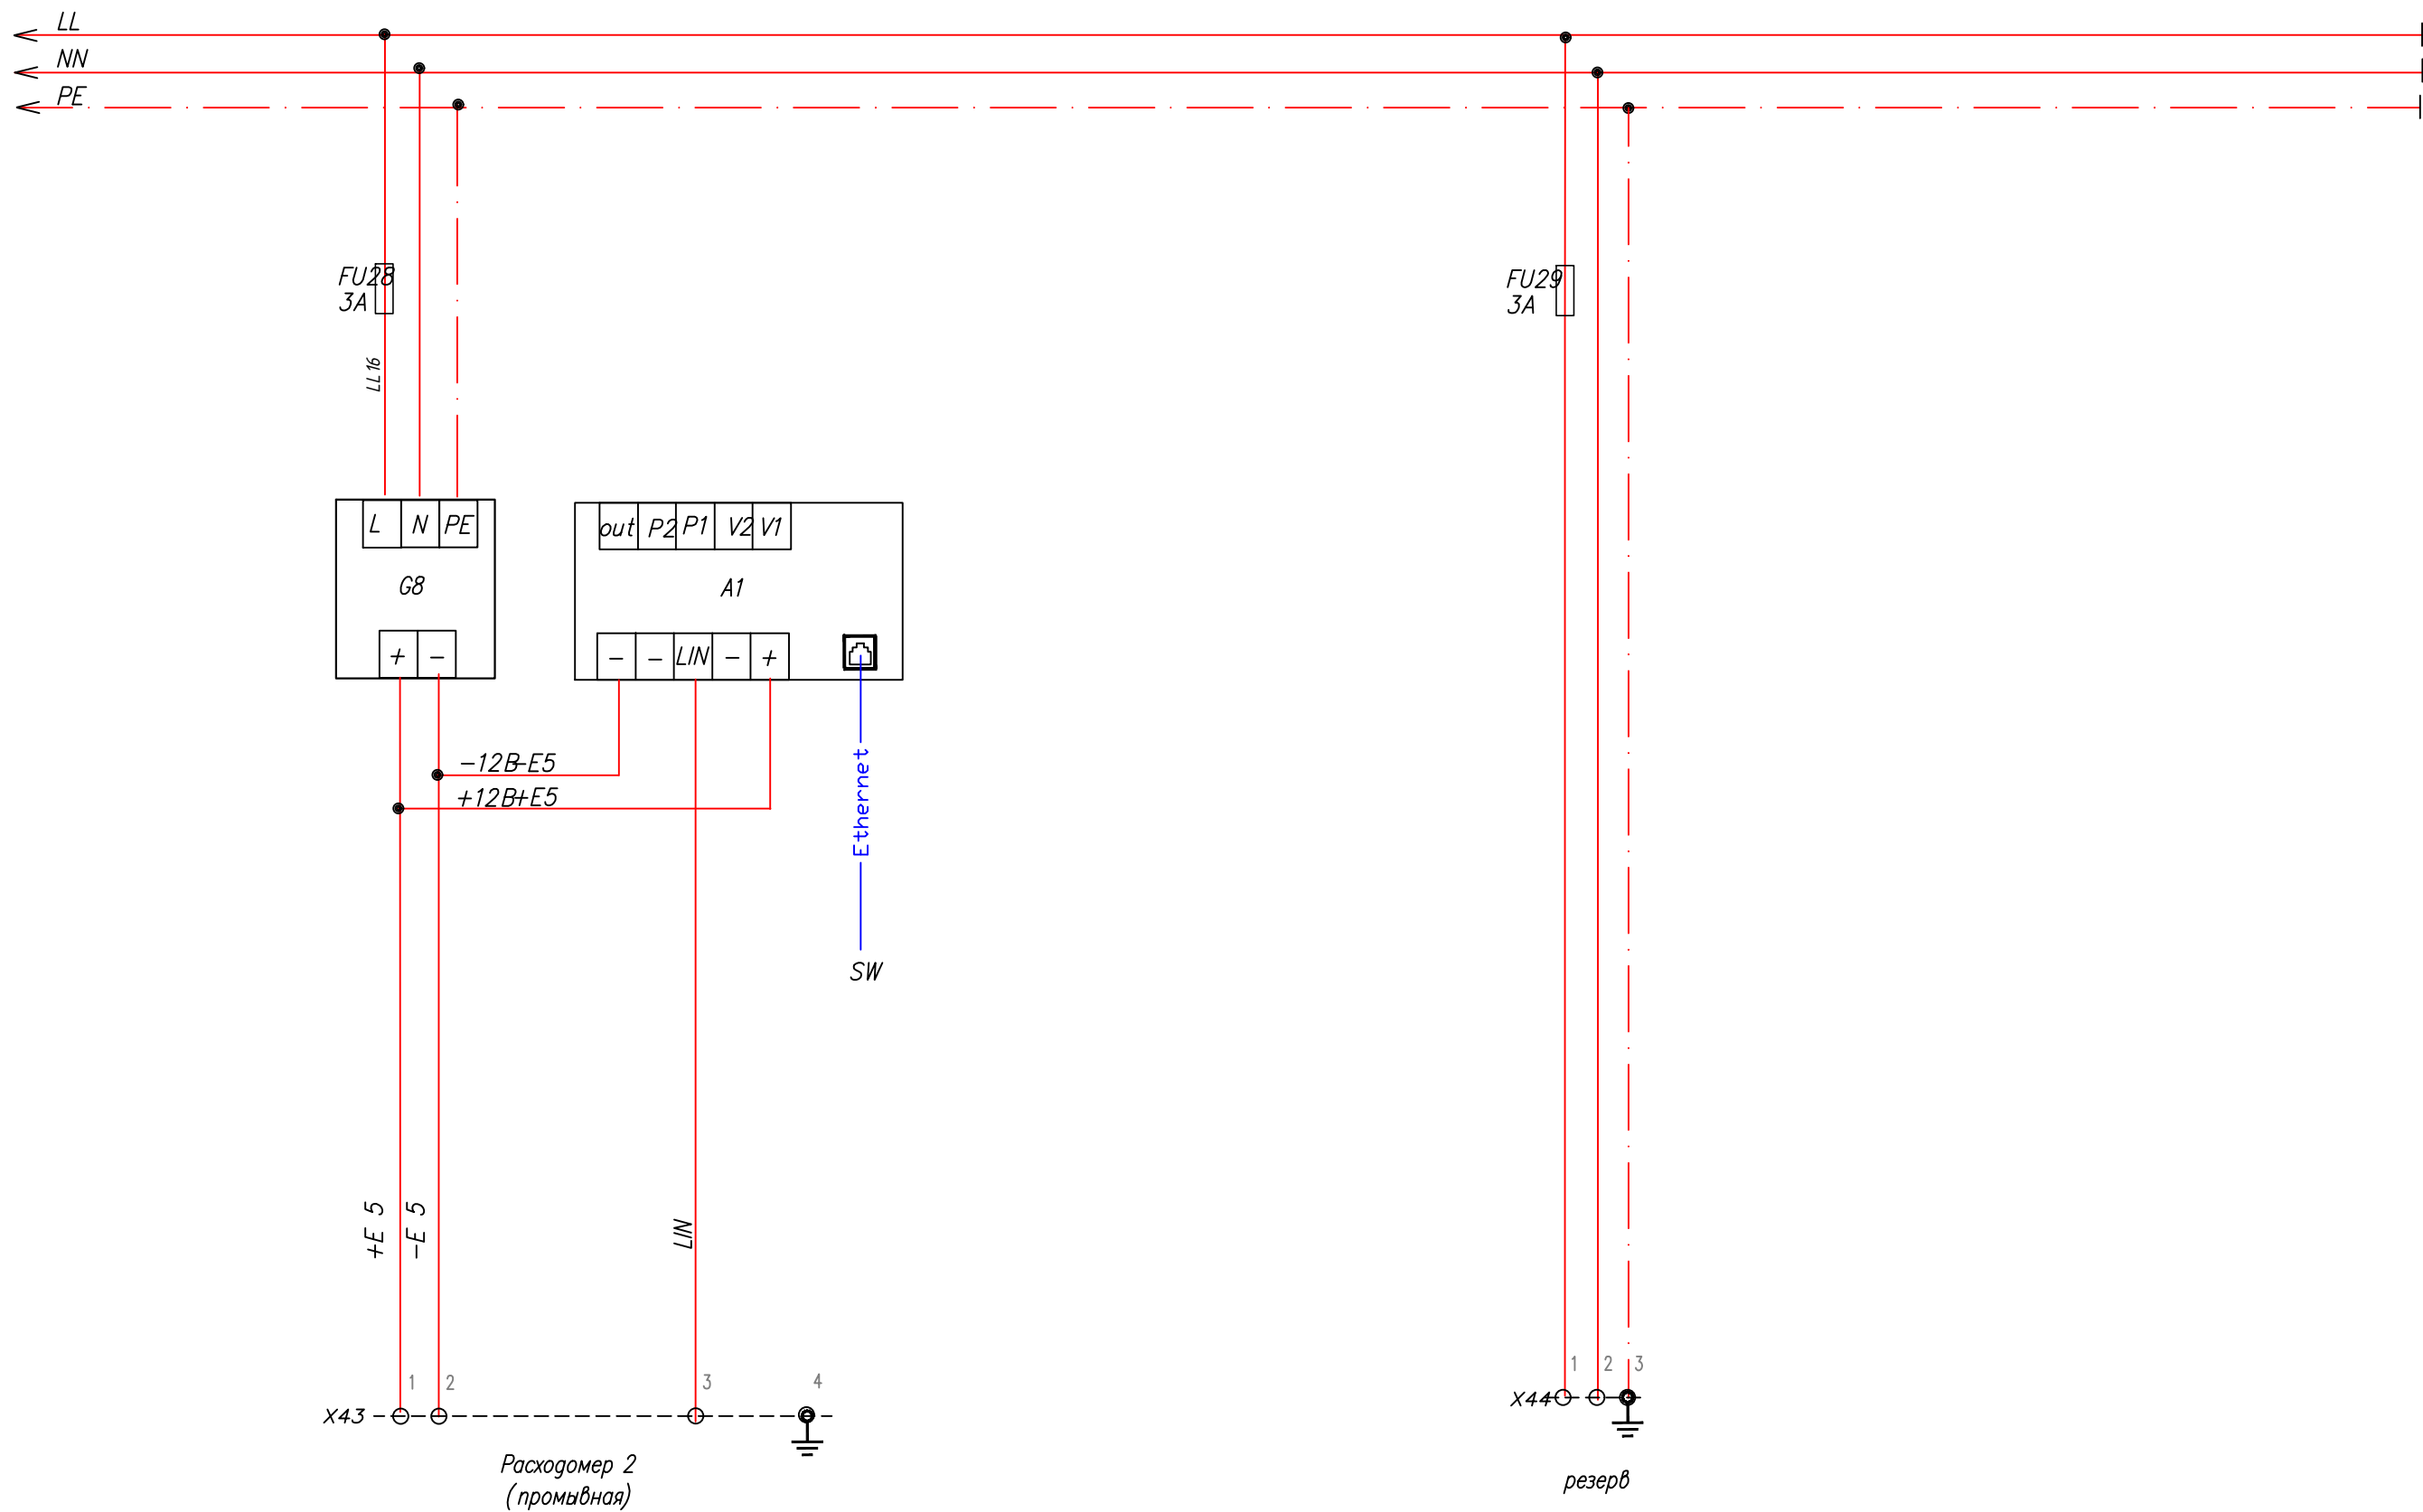

					14192.012/2024-АТХ	Лист
						6.16
Изм	Лист	№ докум	Подпись	Дата		