


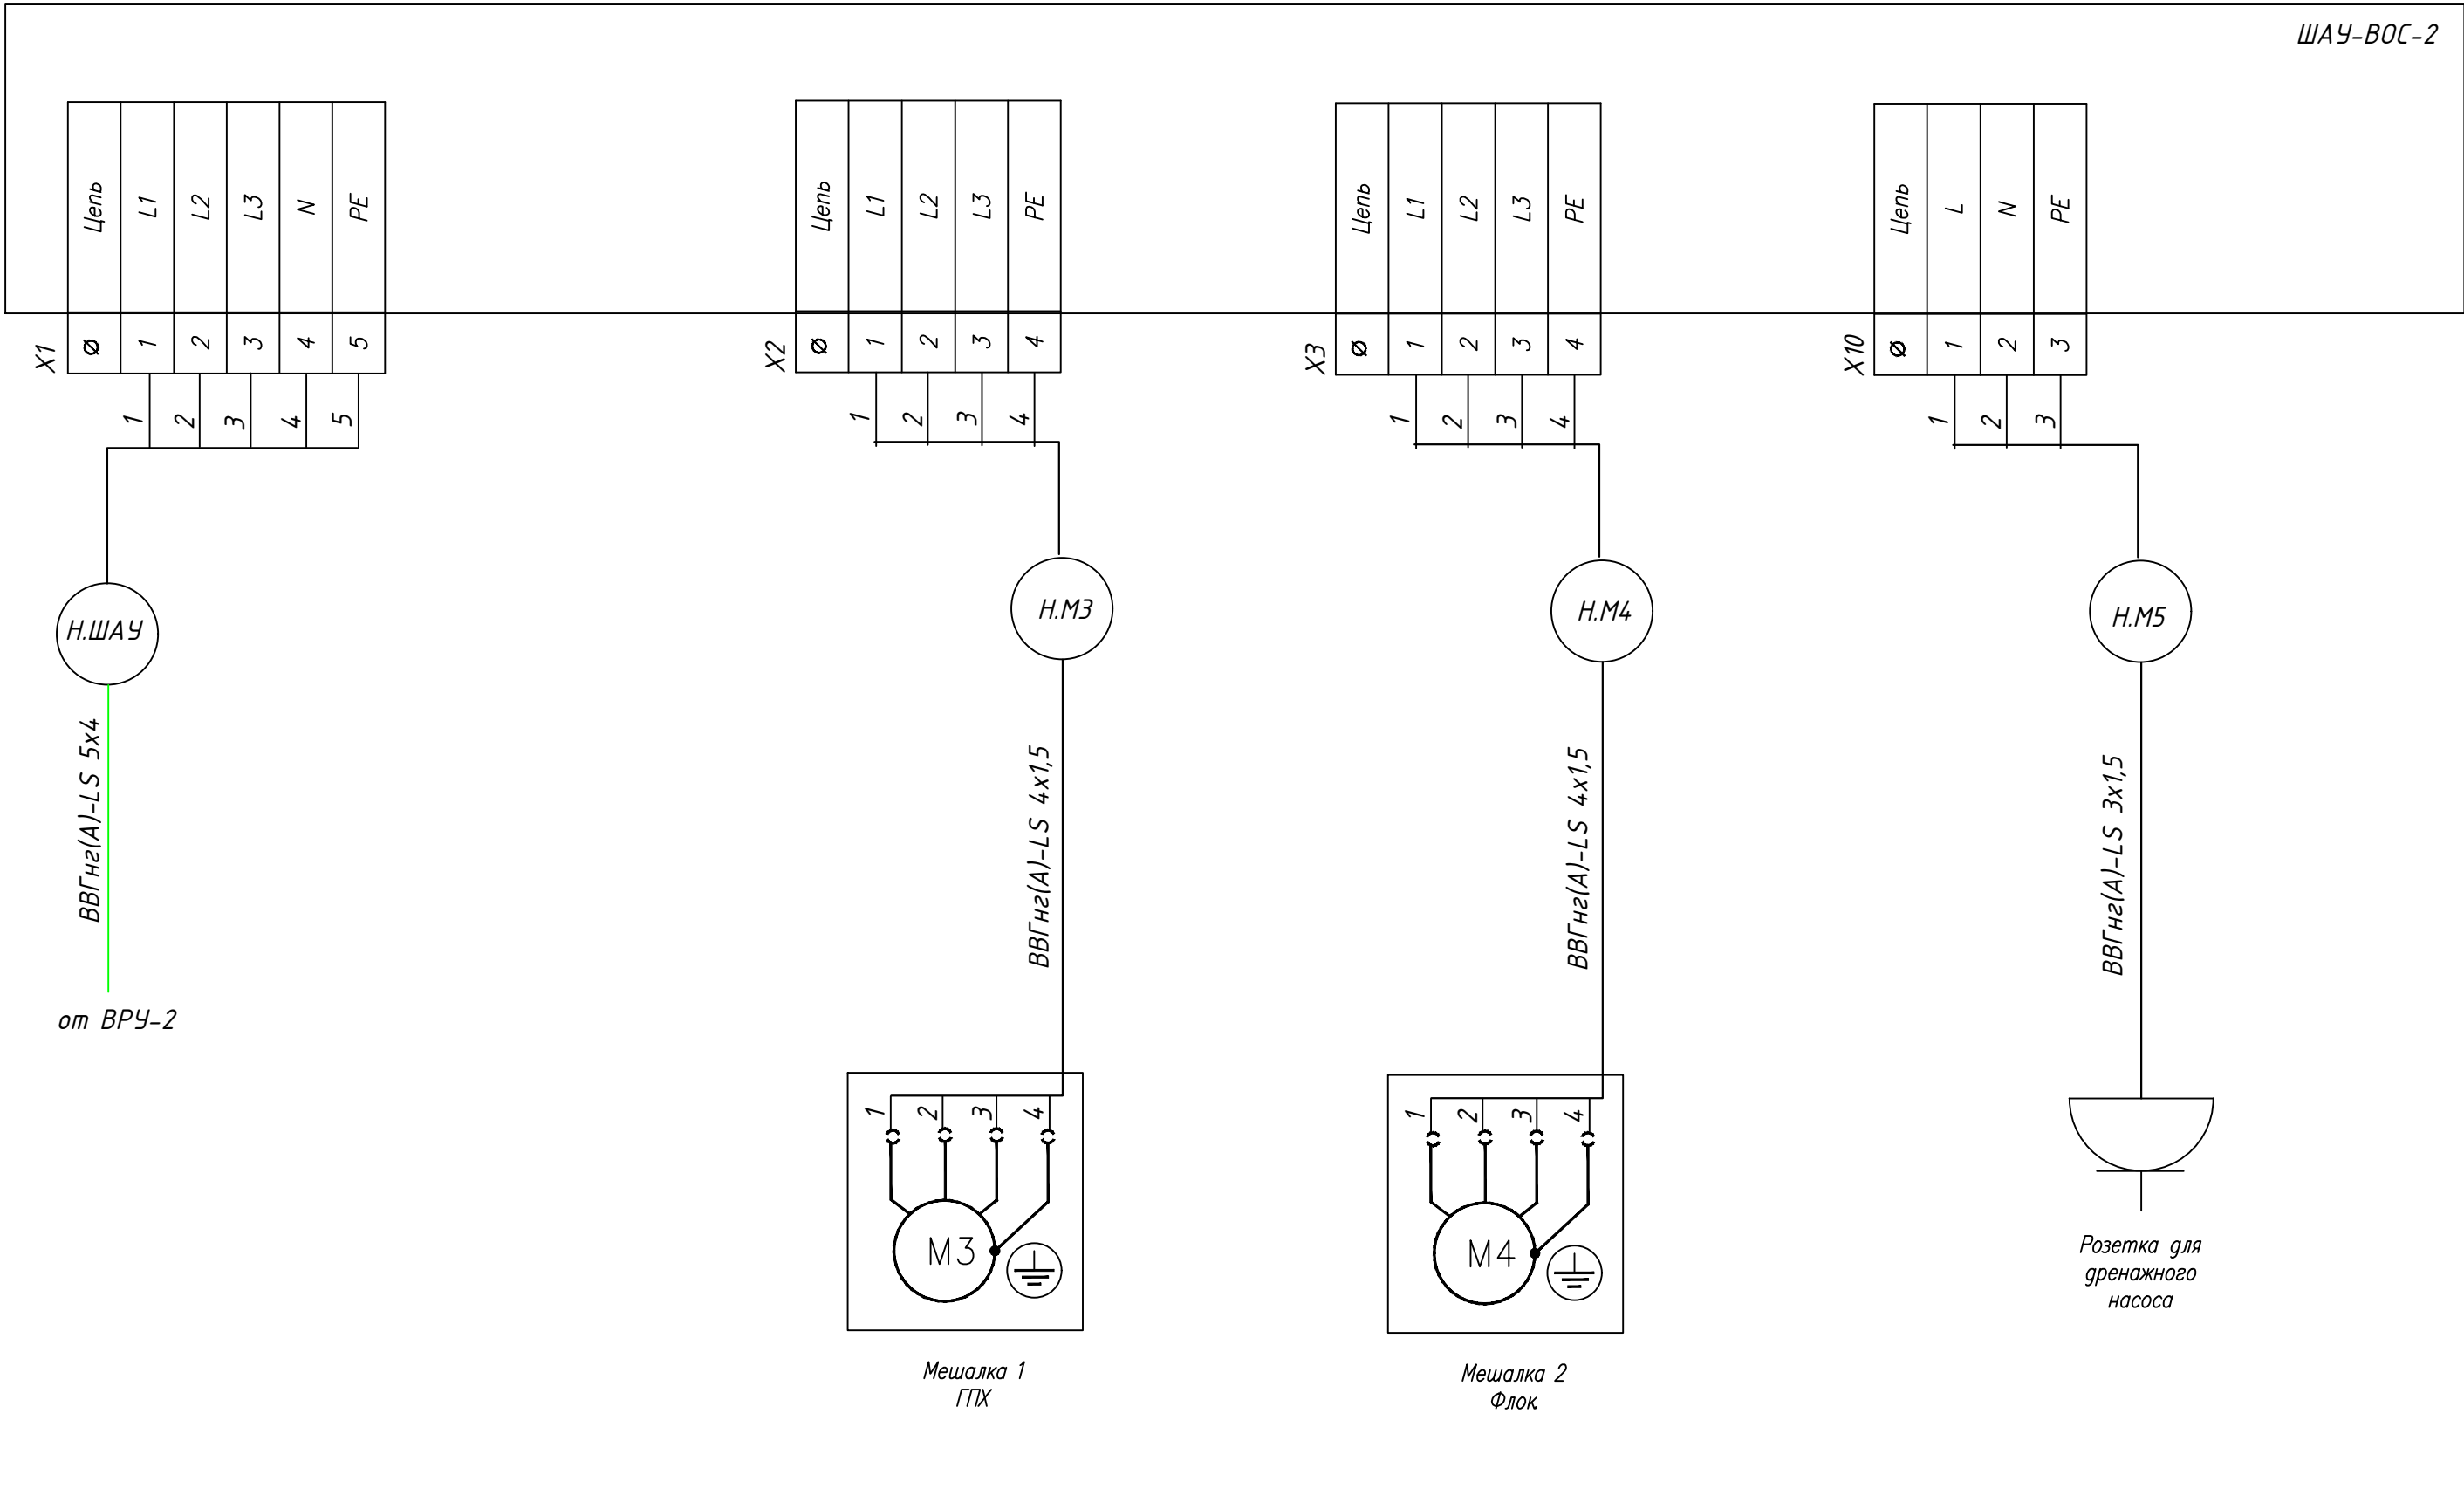

						14 192.012/2024-АТХ			
						«Модернизация объекта «Здание вооочистных сооружений» в с. Панаевск»			
Изм.	Кол.уч.	Лист	N док.	Подп.	Дата	Автоматизация технологии	Стадия	Лист	Листов
Разраб.	Бакланов				04.25		Р	7.1	9
Проверил	Никитин				04.25				
Н. контр.	Шамова				04.25	ШАУ-ВОС-2 Схема внешних соединений	ООО "МСБ"		
ГИП	Усвятцев				04.25				