



	Условные обозначения трубопроводов и потоков:
B10	Трубопровод исходной воды
B20	Трубопровод от контактных колонн к фильтрам I ступени
B30	Трубопровод отфильтрованных вод к фильтрам II ступени
B40	Трубопровод отфильтрованных вод к фильтрам III ступени
B50	Трубопровод обеззараживания и подачи к потребителю
B60H	Напорный трубопровод чистой промывной воды
B70	Трубопровод собственных нужд
B80	Трубопровод отбора проб
K10	Отвод первого фильтрата
K20H	Напорный трубопровод грязной промывной воды
K30	Канализация собственных нужд
P1	Трубопровод гипохлорита натрия
P2	Трубопровод коагулянта
P3	Трубопровод щёлочи
P4	Трубопровод флокулянта

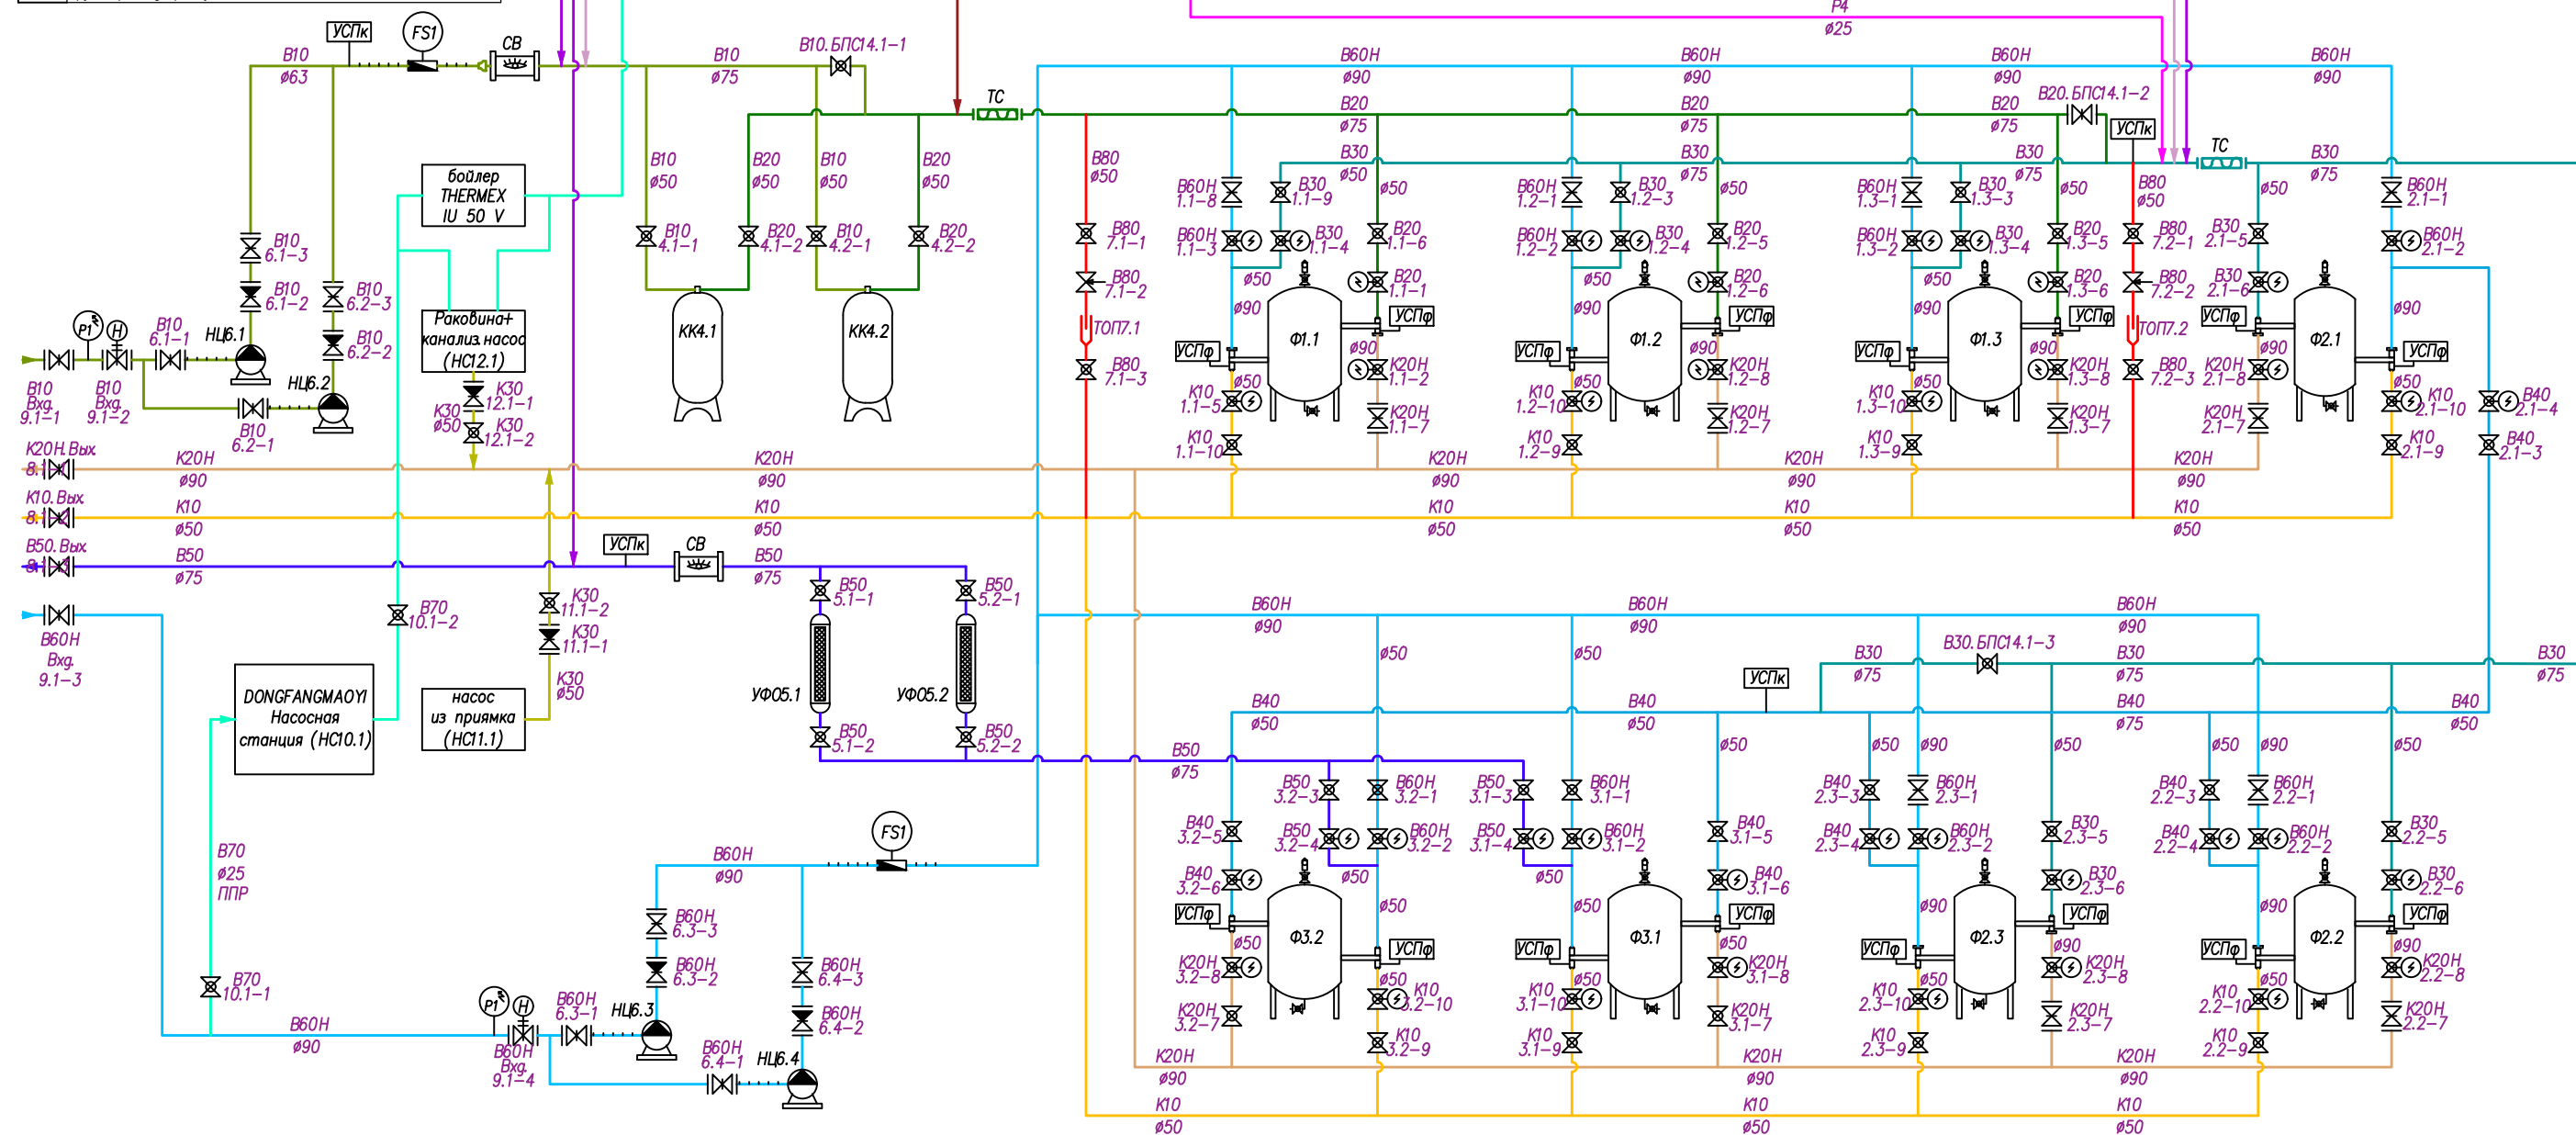

Условное графическое обозначение

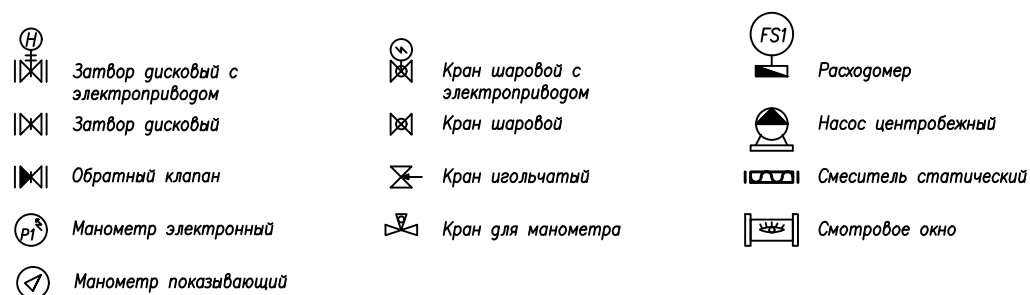

Изм.	Кол.уч	Лист	Ндоп	Подпись	Дата				
Разработал		ФИО 1			12.05.25		Стадия	Лист	Листов
Проверил		ФИО 2			12.05.25				
Н. контр.		ФИО 3			12.05.25				